
Service Tile positions (Pos 1, 2a, 2b ...) per Service Tile Room Overview 14.08.2026, marked outside the building at the module lines - a/b = tiles either side of the same module line. Labels ST-001-174 carry room and position. Position markers added by Kyodo Projects ApS, 07.10.2026.

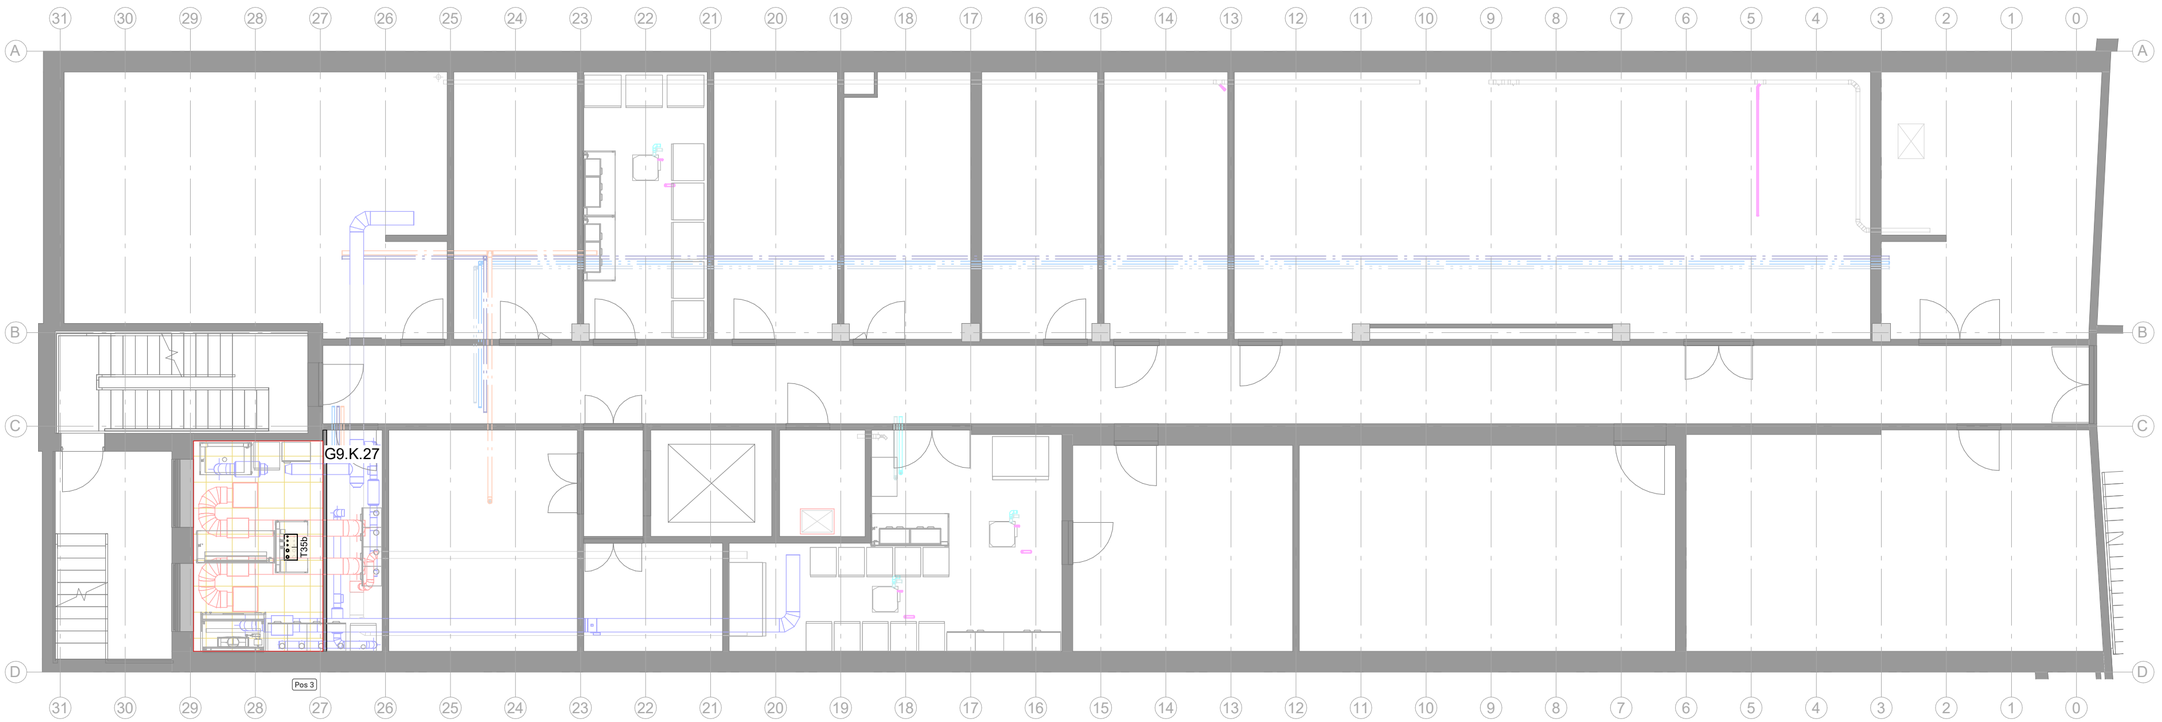

EKL Service Tile Types Plan

1 : 100

Service Tile Type Overview	
Type	Count
Type35b - 2x400V, WPW, WPC, AKW	1
Grand total: 1	

Service tile Type Legend

- Type 01: 1x400V
- Type 02: 2x400V
- Type 03: 1x400V, 1xSingle Data
- Type 04: 2x400V, 1xDouble Data
- Type 11: 1xVAC
- Type 12: 1xCA
- Type 21: 1x400V 1xVAC
- Type 22: 1x400V 1xCO_2
- Type 23: 1x400V 1xVAC, 1xCA
- Type 24: 1x400V, 1xSingle Data 1xCA
- Type 25: 1x400V, 1xDouble Data 1xVAC
- Type 26: 2x400V, 1xDouble Data 1xCA
- Type 27: 2x400V, 1xDouble Data 1xVAC, 1xCA
- Type 31: 1x400V 1xWPC, 1xWPW
- Type 32: 2x400V 1xWPC
- Type 33: 1x400V 1xWPC, 1xWPW, 1xAKW
- Type 34: 2x400V, 1xDouble Data 1xWPC, 1xWPW
- Type 35: 2x400V 1xWPC, 1xWPW, 1xAKW
- Type 36: 2x400V 1xWPC, 1xWPW
- Type Kontor: 1x400V, 1xDouble Data

REV.	DATE	DESCRIPTION	BY

PROJECT ADDRESS: Måløv B G9			
PROJECT NUMBER: **251201**	PROJECT PHASE: **DD**		
PROJECT NAME: **NN G9**	SHEET FORMAT: A2 Landscape	SCALE: As indicated	
DRAWING TITLE: Service Tile - Basement	DRAWN: GL	CHECKED: MS	APPROVED: DS
DRAWING NUMBER: **MAA G9 02 DD 35 000011**	REV.	DATE: **04/06/2025**	
CLIENT: **Novo Nordisk** Client name	kyodo.dk	1 inch	10 mm