
Service Tile positions (Pos 1, 2a, 2b ...) per Service Tile Room Overview 14.08.2026, marked outside the building at the module lines - a/b = tiles either side of the same module line. Labels ST-001-174 carry room and position. Position markers added by Kyodo Projects ApS, 07.10.2026.

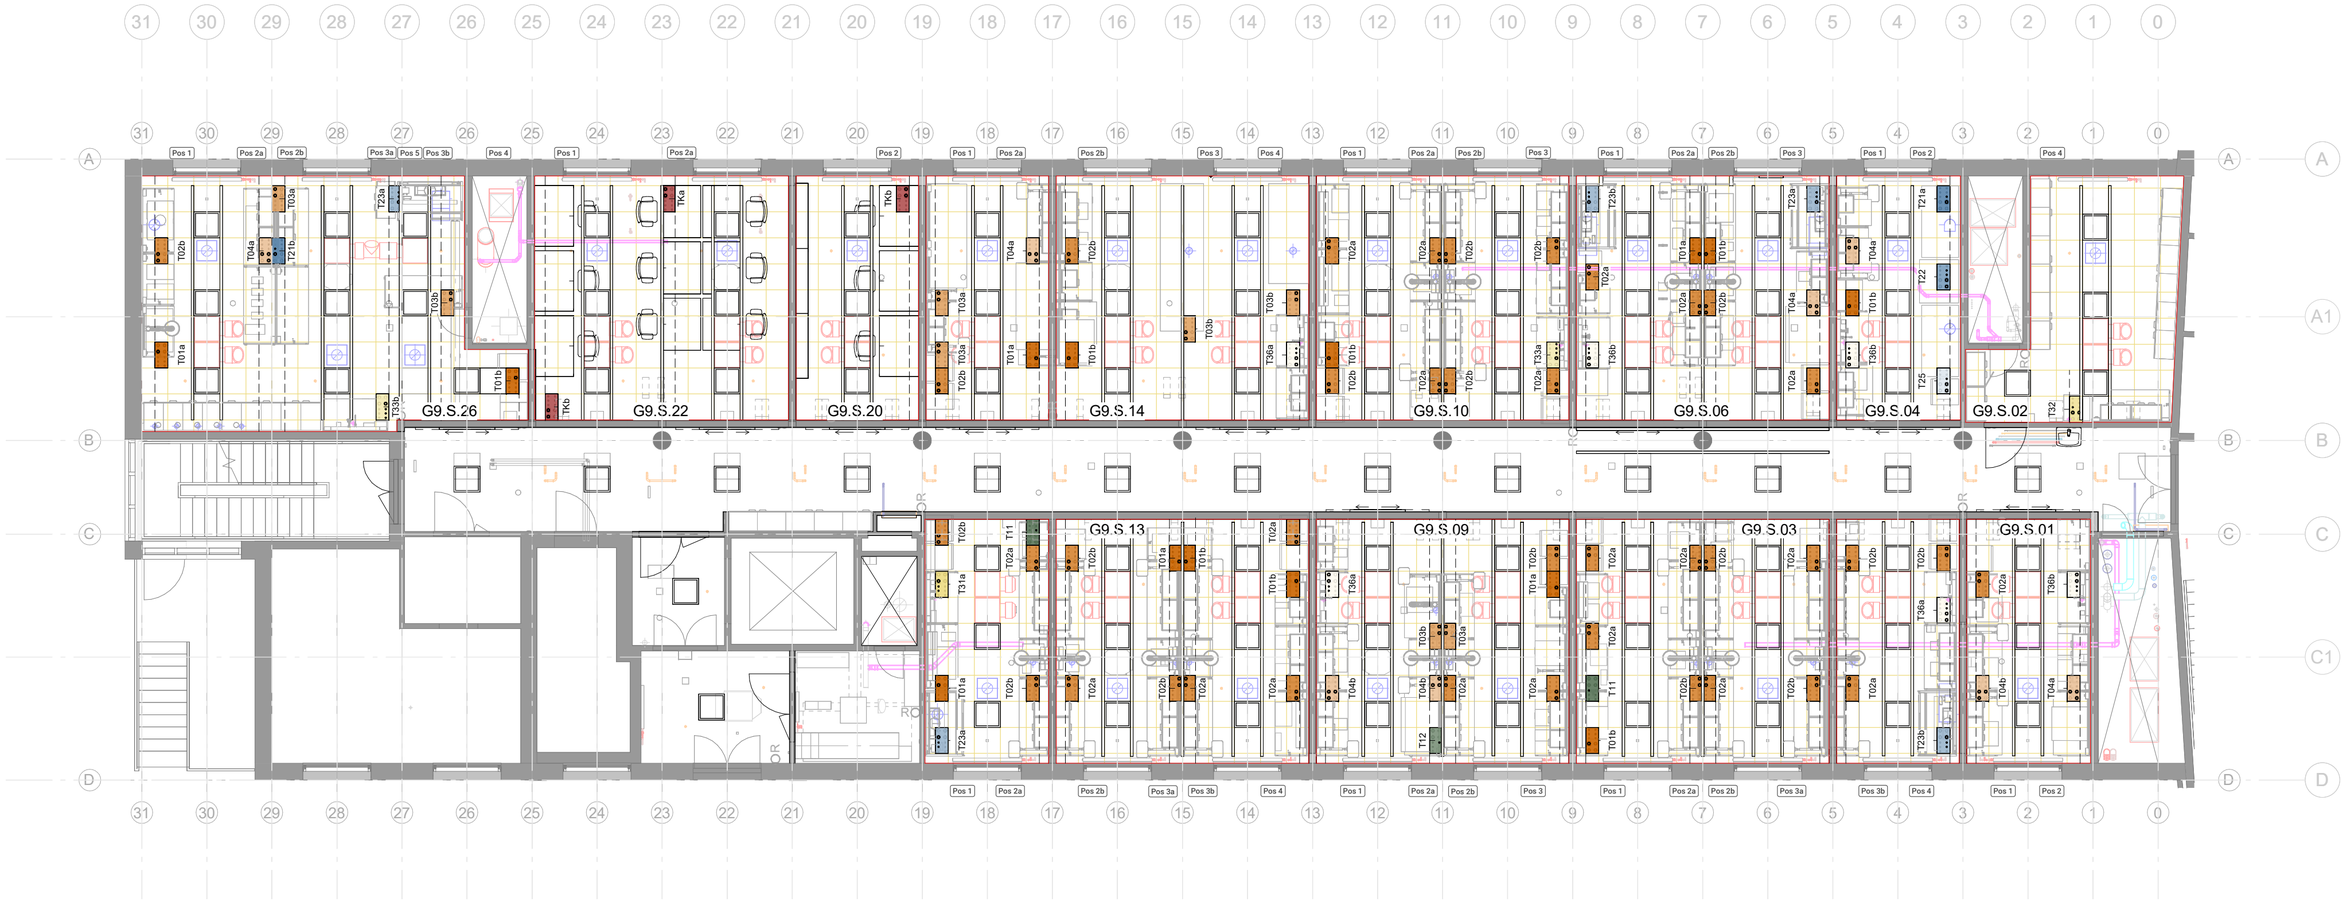

Service Tile Type Overview	
Type	Count
Type01a - 1x400V	6
Type01b - 1x400V	8
Type02a - 2x400V	21
Type02b - 2x400V	18
Type03a - 1x400V, 1xDoubleData	4
Type03b - 1x400V, 1xDoubleData	4
Type04a - 2x400V, 1xDoubleData	5
Type04b - 2x400V, 1xDoubleData	3

Service Tile Type Overview	
Type	Count
Type11 - V	2
Type12 - CA	1

Service Tile Type Overview	
Type	Count
Type21a - 1x400V, V	1
Type21b - 1x400V, V	1
Type22 - 2x400V, 2xCO2	1
Type23a - 1x400V, V, CA	3
Type23b - 1x400V, VA CA	2
Type25 - 2x400V, V	1

Service Tile Type Overview	
Type	Count
Type31a - 1x400V, WPC, WPH	1
Type32 - 2x400V, WPC	1
Type33a - 1x400V, WPC, WPH, WDI	1
Type33b - 1x400V, WPC, WPH, WDI	1
Type36a - 2x400V, WPC, WPH	3
Type36b - 2x400V, WPC, WPH	3

Service Tile Type Overview	
Type	Count
Type Kontor a - 1x400V, 1xDoubleData	1
Type Kontor b - 1x400V, 1xDoubleData	2
Grand total: 94	

Service tile Type Legend

- Type 01: 1x400V
- Type 02: 2x400V
- Type 03: 1x400V, 1xDouble Data
- Type 04: 2x400V, 1xDouble Data
- Type 11: 1xV
- Type 12: 1xCA
- Type 21: 1x400V 1xV
- Type 22: 2x400V 2xCO_2
- Type 23: 1x400V 1xV, 1xCA
- Type 24: 1x400V, 1xDouble Data 1xCA
- Type 25: 2x400V 1xV
- Type 26: 2x400V, 1xDouble Data 1xCA
- Type 27: 2x400V, 1xDouble Data 1xV, 1xCA
- Type 31: 1x400V 1xWPC, 1xWPH
- Type 32: 2x400V 1xWPC
- Type 33: 1x400V 1xWPC, 1xWPH, 1xWDI
- Type 34: 2x400V, 1xDouble Data 1xWPC, 1xWPH
- Type 35: 2x400V 1xWPC, 1xWPH, 1xWDI
- Type 36: 2x400V 1xWPC, 1xWPH
- Type Kontor: 1x400V, 1xDouble Data

LEGEND

V	- Vacuum
CA	- Compressed Air
CO2	- Carbon dioxide
WPC	- Cold water, Potable
WPH	- Warm water, Potable
WDI	- Special water (AKW)
400V 16A	- CEE socket for 400V 16A
Double Data	- 2pcs. FCC socket outlets

REV.	DATE	DESCRIPTION	BY

PROJECT ADDRESS: Måløv B G9

PROJECT NUMBER: **251201**		PROJECT PHASE: **DD**	
PROJECT NAME: **NN G9**		SHEET FORMAT: A2 Landscape	SCALE: As indicated
DRAWING TITLE: Service Tile - Ground Floor		DRAWN: GL	CHECKED: MS / APPROVED: DS
DRAWING NUMBER: **MAA G9 02 DD 35 000021**	REV.	DATE: **26/06/2026**	
CLIENT: **Novo Nordisk**		kyodo lab — kyodo.dk — 1 inch — 10 mm	