
Service Tile positions (Pos 1, 2a, 2b ...) per Service Tile Room Overview 14.08.2026, marked outside the building at the module lines - a/b = tiles either side of the same module line; two numbers in one marker = two rows of tiles at that module position. Position markers added by Kyodo Projects ApS, 07.10.2026.

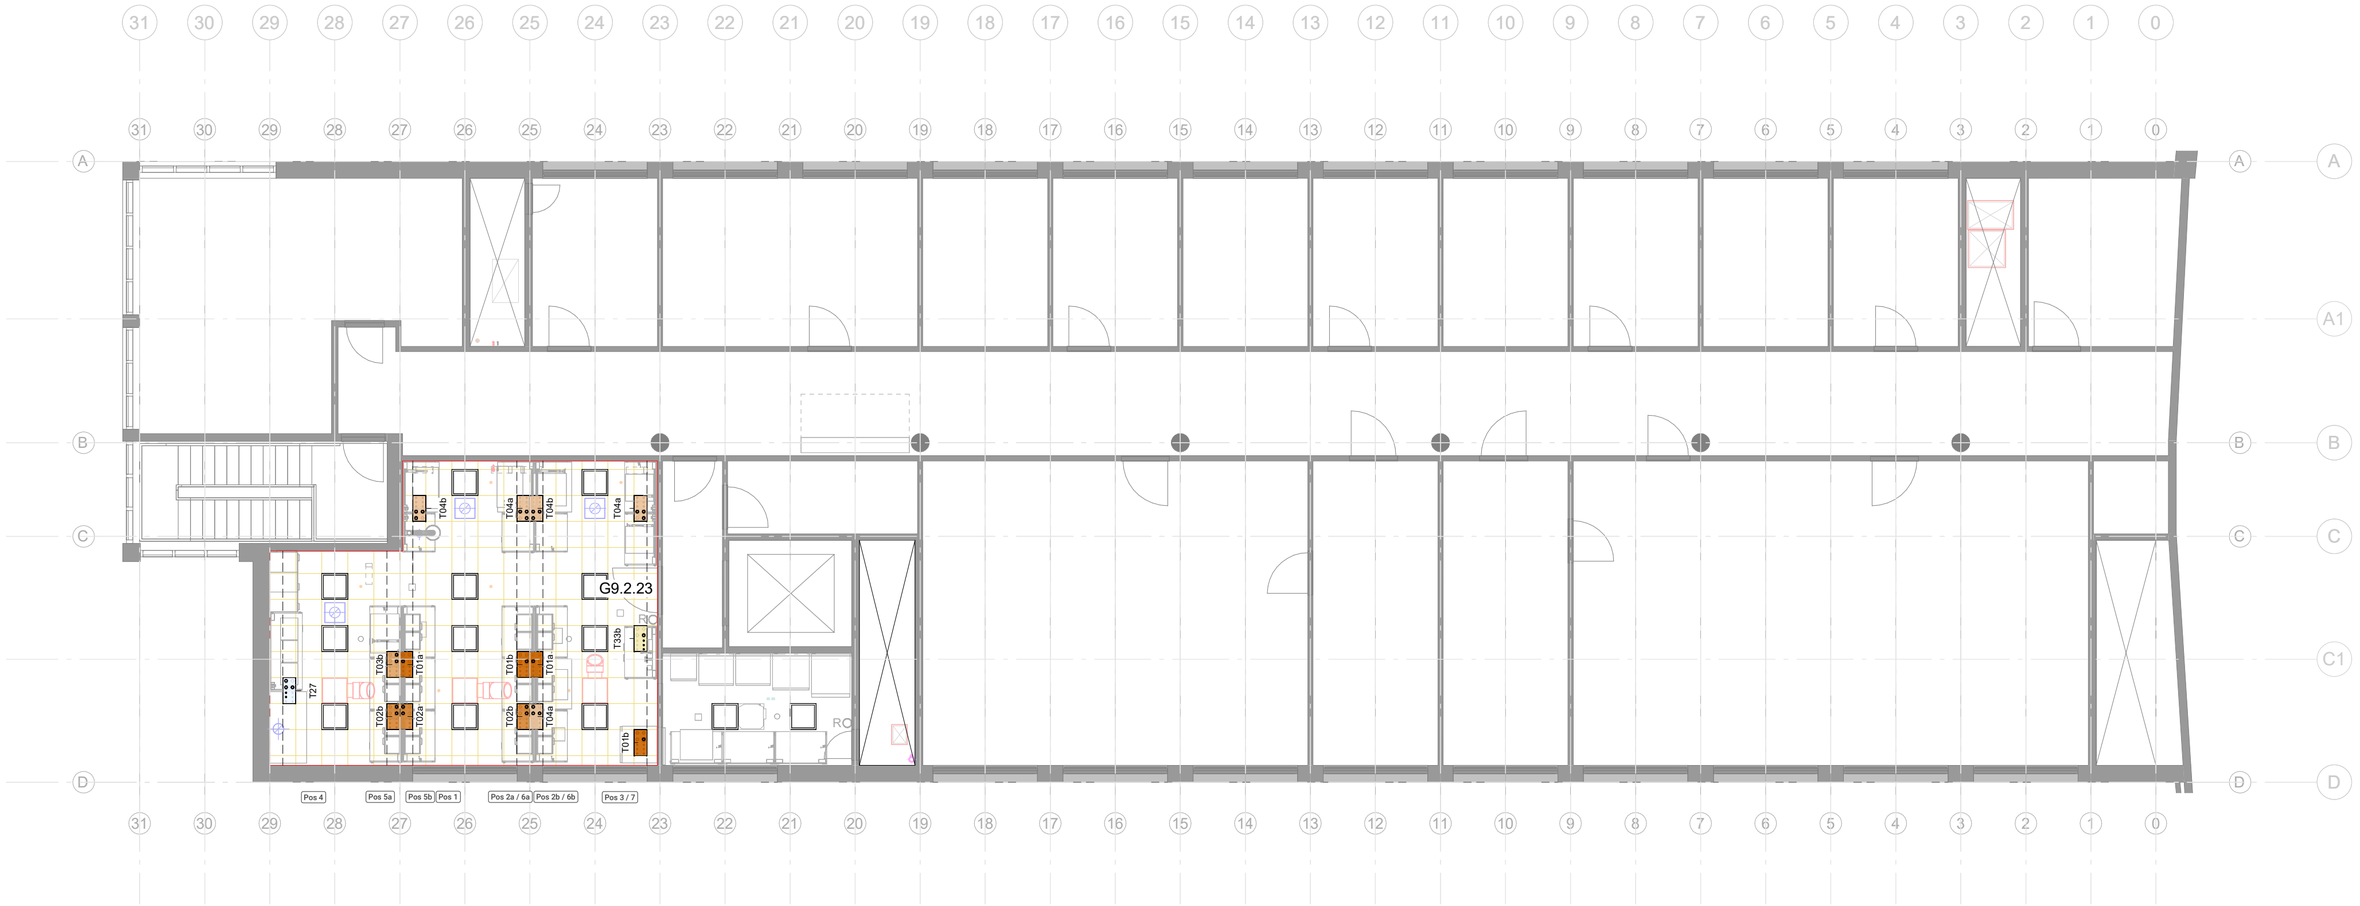

Service Tile Type Overview	
Type	Count
Type01a - 1x400V	2
Type01b - 1x400V	2
Type02a - 2x400V	1
Type02b - 2x400V	2
Type03b - 1x400V, 1xDoubleData	1
Type04a - 2x400V, 1xDoubleData	3
Type04b - 2x400V, 1xDoubleData	2

Service Tile Type Overview	
Type	Count
Type27 - 2x400V, 1xDoubleData, V, CA	1

Service Tile Type Overview	
Type	Count
Type33b - 1x400V, WPC, WPH, WDI	1
Grand total: 15	

Service tile Type Legend

- Type 01: 1x400V
- Type 02: 2x400V
- Type 03: 1x400V, 1xDouble Data
- Type 04: 2x400V, 1xDouble Data
- Type 11: 1xV
- Type 12: 1xCA
- Type 21: 1x400V 1xV
- Type 22: 2x400V 2xCO_2
- Type 23: 1x400V 1xV, 1xCA
- Type 24: 1x400V, 1xDouble Data 1xCA
- Type 25: 2x400V 1xV
- Type 26: 2x400V, 1xDouble Data 1xCA
- Type 27: 2x400V, 1xDouble Data 1xV, 1xCA
- Type 31: 1x400V 1xWPC, 1xWPH
- Type 32: 2x400V 1xWPC
- Type 33: 1x400V 1xWPC, 1xWPH, 1xWDI
- Type 34: 2x400V, 1xDouble Data 1xWPC, 1xWPH
- Type 35: 2x400V 1xWPC, 1xWPH, 1xWDI
- Type 36: 2x400V 1xWPC, 1xWPH
- Type Kontor: 1x400V, 1xDouble Data

LEGEND

V	- Vacuum
CA	- Compressed Air
CO2	- Carbon dioxide
WPC	- Cold water, Potable
WPH	- Warm water, Potable
WDI	- Special water (AKW)
400V 16A	- CEE socket for 400V 16A
Double Data	- 2pcs. FCC socket outlets

REV.	DATE	DESCRIPTION	BY

PROJECT ADDRESS: Måløv B G9

PROJECT NUMBER	PROJECT PHASE		
251201	DD		
PROJECT NAME	SHEET FORMAT	SCALE	
NN G9	A2 Landscape	As indicated	
DRAWING TITLE	DRAWN	CHECKED	APPROVED
Service Tile - 2nd Floor	GL	MS	DS
DRAWING NUMBER	REV.	DATE	
MAA G9 02 DD 35 000041		26/06/2026	

CLIENT: Novo Nordisk

kyodo.dk 1 inch 10 mm